

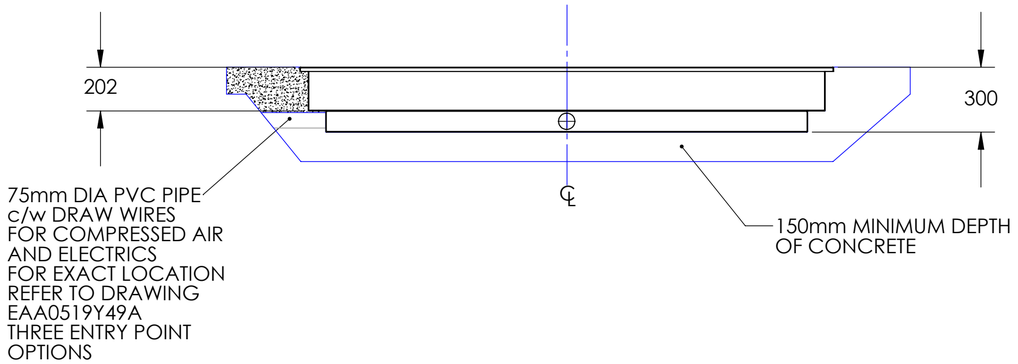


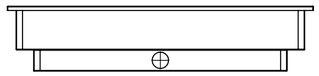

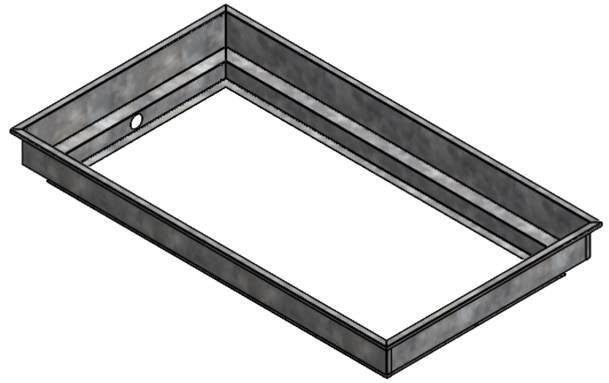

NOTES:


1, ELECTRICAL SUPPLY TO BE SUPPLIED BY CUSTOMER
NEXT TO COMPUTER.

SINGLE PHASE, 240 VOLTS, 50Hz, 13 AMP TWIN SWITCHED SOCKET


2, FLOOR TO BE SUBSTANTIALLY LEVEL ACROSS BAY +/-5MM


3, PULL CABLE TO BE LEFT IN SERVICE DUCT FROM COMPUTER
TO TYRE TREAD READER BED.

4, INTERNALY BRACE PIT WALLS WHILE CONCREATE IS SETTING.

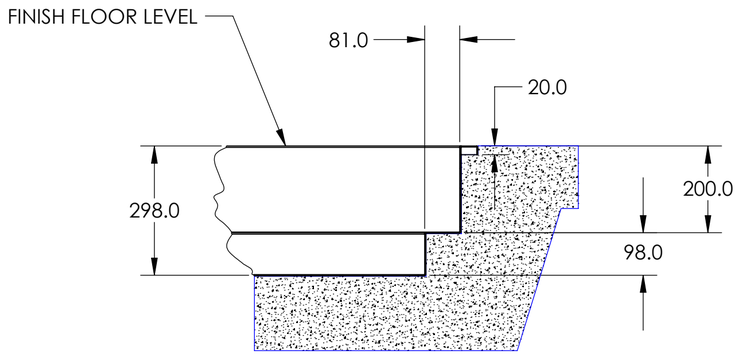

DETAIL B
SCALE 1 : 10
ALL DIMENSIONS ARE INTERNAL

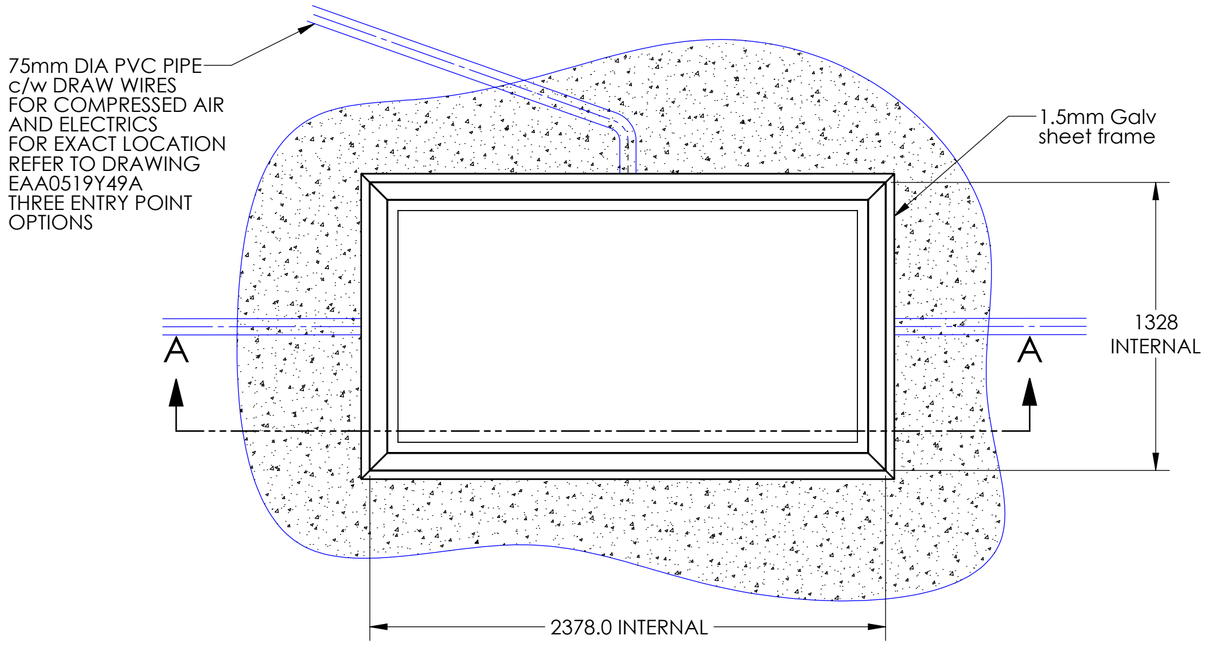

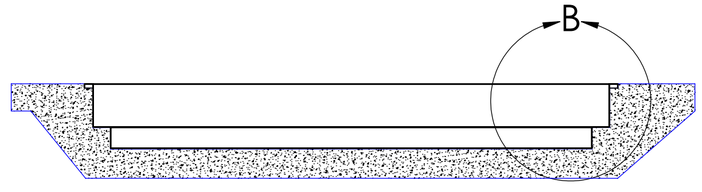

SECTION A-A

ALL MATERIALS MUST COMPLY WITH ROHS, REACH, CA PROP65, AND CONFLICT MINERALS.

UNLESS OTHERWISE SPECIFIED:
DIMENSIONS ARE IN MILLIMETERS
TOLERANCES:
LINEAR: 1 PLACE ± 0.25
2 PLACES ± 0.10
ANGULAR: ± 0.5

FINISH: CLEAN

DEBUR AND BREAK SHARP EDGES

DO NOT SCALE DRAWING | THIRD ANGLE PROJECTION

	NAME	DATE	ISSUE	MODIFICATIONS
DRAWN	SL	8/4/2021	1	INITIAL RELEASE
CHK'D				
APPV'D				
MFG				
Q.A				

MATERIAL: Galvanized Steel

Snap-on

TITLE: GROUND WORKS DETAIL

DWG NO. EAZ0155Y00A | A2

SCALE:1:20 | SHEET 1 OF 1

THE DATA, DRAWINGS, AND INFORMATION CONTAINED IN THIS DOCUMENT IS CONFIDENTIALAND THE SOLE PROPERTY OF SNAP-ON, AND MAY NOT BE REPRODUCED, USED, OR DISCLOSED WITHOUT WRITTEN PERMISSION OF AN OFFICER OF SNAP-ON